SAMPLE: WALLER GARDEN APARTMENTS

SCHEMATIC DESIGN SET — OPTION A

Amenity / commons · Multifamily · Sample site (anonymized), Waller · Waller County · 15.97 acres



SITE KEY PLAN · not to scale · see C-101

PROJECT DATA

Gross site area	15.97 ac	695,836 sf
Building footprint (all uses)	145,470 sf	20.9%
Impervious (buildings + paving)	9.60 ac	60.1%
Detention / pond	2.02 ac	12.6%
Landscape / open space	4.36 ac	27.3%
Floor area / FAR	425,611 sf	0.61
Dwelling units / gross density	389 du	24.4 du/ac

PROGRAM & PARKING

USE	SIZE	FLOORS
Amenity / commons — Clubhouse	5,400 sf	1
Multifamily — 13 bldgs	389 du · 420,211 sf	3
Surface stalls (counted on plan)	657	
Accessible (ADA) stalls, in the total	14 (3 van)	
Total provided	657	
Needed at the ratios used	623	

SHEET INDEX

GENERAL	
G-001	Cover sheet
SITE & CIVIL	
C-101	Overall site plan

PROJECT TEAM

Owner / client	Finishes Solutions (sample)
Development consultant	Finishes Solutions
Architect of record	To be engaged
Civil engineer	To be engaged
Structural engineer	To be engaged
MEP engineer	To be engaged
Surveyor	To be engaged
Geotechnical engineer	To be engaged

GENERAL NOTES

The notes weren't written for this issue (the AI wasn't available). The drawings and numbers are complete.

TEL: 936-372-1670

Finishes SOLUTIONS LLC.

1004 PRIYA LN., WALLER, TX 77484

PROJECT
SAMPLE: WALLER GARDEN APARTMENTS
Sample site (anonymized), Waller
Waller County · 15.97 acres

PREPARED FOR
Finishes Solutions (sample)

PREPARED BY
Finishes Solutions

PHASE
Schematic design · Option A

DATE
2026-10-24

SCALE
As noted

PRELIMINARY — NOT FOR CONSTRUCTION, BIDDING OR PERMIT.

Schematic design drawings prepared by Finishes Solutions from a conceptual site plan, with AI assistance, for feasibility, pricing and coordination only. Not prepared or sealed by a licensed architect, engineer or surveyor. Boundary, easements, utilities, drainage, structure and code compliance are not verified and must be designed, verified and sealed by licensed professionals before construction or permitting.

ISSUE/REVISION NO.	DATE:	DESCRIPTION:

DRAWN BY:

CHECKED BY:


PROJECT NUMBER:

SHEET TITLE
COVER SHEET
Sheet index · Project data · Notes

SHEET NUMBER

G-001

FINISHES SOLUTIONS LLC. ALL RIGHTS RESERVED

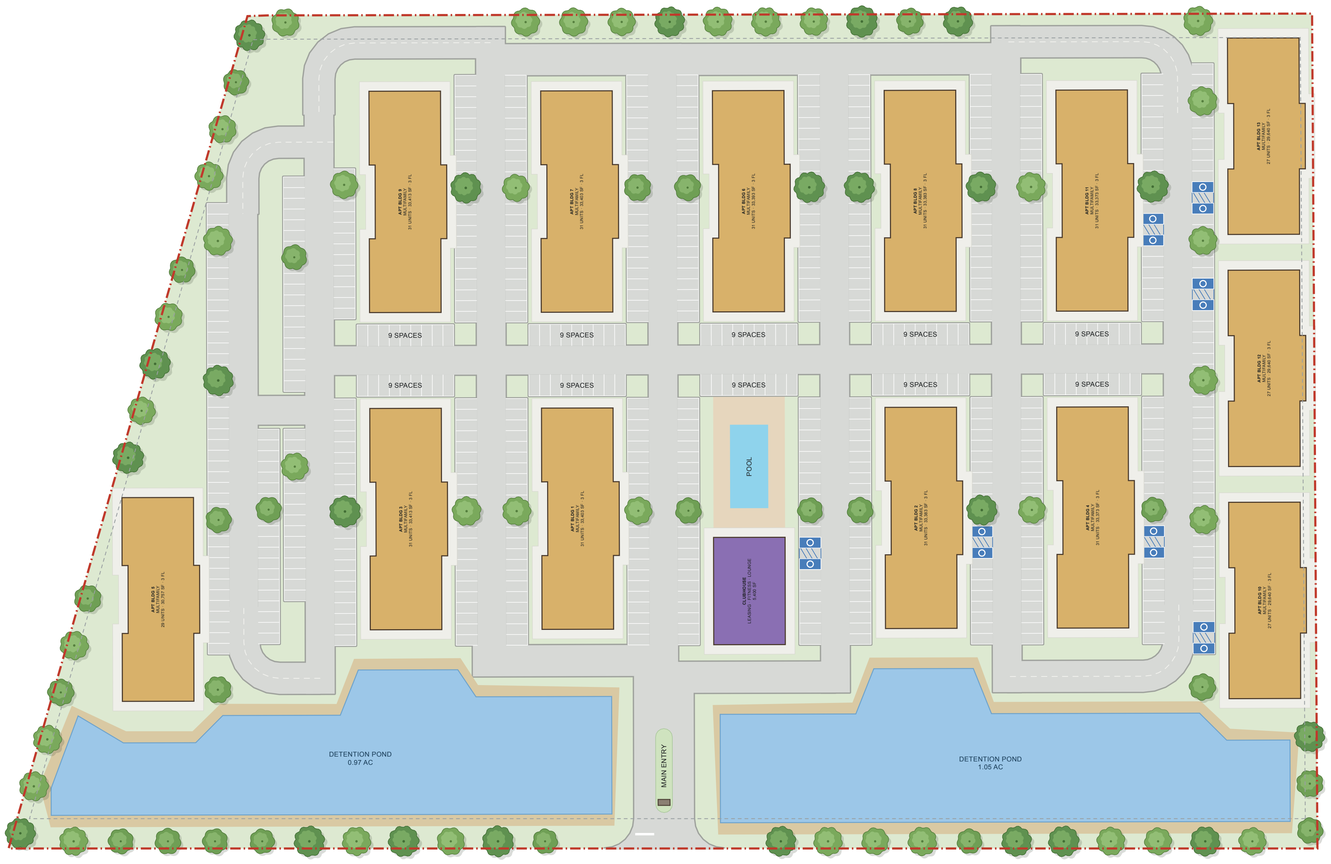

1 **OVERALL SITE PLAN**
Scale: 1" = 60'-0" on 24" × 36"

0' 30' 60' 120'

LEGEND

- Apartments
- Community / amenity building
- Asphalt / concrete paving
- Detention / amenity lake
- Landscape / open space
- Accessible (ADA) stall
- Monument sign
- Canopy tree (proposed)
- Boundary
- Building setback

SITE DATA & LAND USE

Gross site area	15.97 ac	695,836 sf
Building footprint (all uses)	145,470 sf	20.9%
Impervious (buildings + paving)	9.60 ac	60.1%
Detention / pond	2.02 ac	12.6%
Landscape / open space	4.36 ac	27.3%
Floor area / FAR	425,611 sf	0.61
Dwelling units / gross density	389 du	24.4 du/ac

PROGRAM & PARKING

USE	SIZE	FLOORS
Amenity / commons — Clubhouse	5,400 sf	1
Multifamily — 13 bldgs	389 du · 420,211 sf	3
Surface stalls (counted on plan)	657	
Accessible (ADA) stalls, in the total	14 (3 van)	
Total provided	657	
Needed at the ratios used	623	

NOTES

1. Boundary from county appraisal district parcel outlines; a boundary and topographic survey is required before design.
2. Building sizes, unit and stall counts are measured from this plan.

Finishes SOLUTIONS LLC.
TEL: 936-372-1670
1004 PRIYA LN., WALLER, TX 77484

PROJECT
SAMPLE: WALLER GARDEN APARTMENTS
Sample site (anonymized), Waller
Waller County · 15.97 acres

PREPARED FOR
Finishes Solutions (sample)

PREPARED BY
Finishes Solutions

PHASE
Schematic design · Option A

DATE
2026-10-24

SCALE
1" = 60'-0"

PRELIMINARY — NOT FOR CONSTRUCTION, BIDDING OR PERMIT.
Schematic design drawings prepared by Finishes Solutions from a conceptual site plan, with AI assistance, for feasibility, pricing and coordination only. Not prepared or sealed by a licensed architect, engineer or surveyor. Boundary, easements, utilities, drainage, structure and code compliance are not verified and must be designed, verified and sealed by licensed professionals before construction or permitting.

ISSUE/REVISION NO.	DATE:	DESCRIPTION:

DRAWN BY:
CHECKED BY:
PROJECT NUMBER:

SHEET TITLE
OVERALL SITE PLAN
Land use · Circulation · Program · Parking

SHEET NUMBER
C-101

FINISHES SOLUTIONS LLC. ALL RIGHTS RESERVED